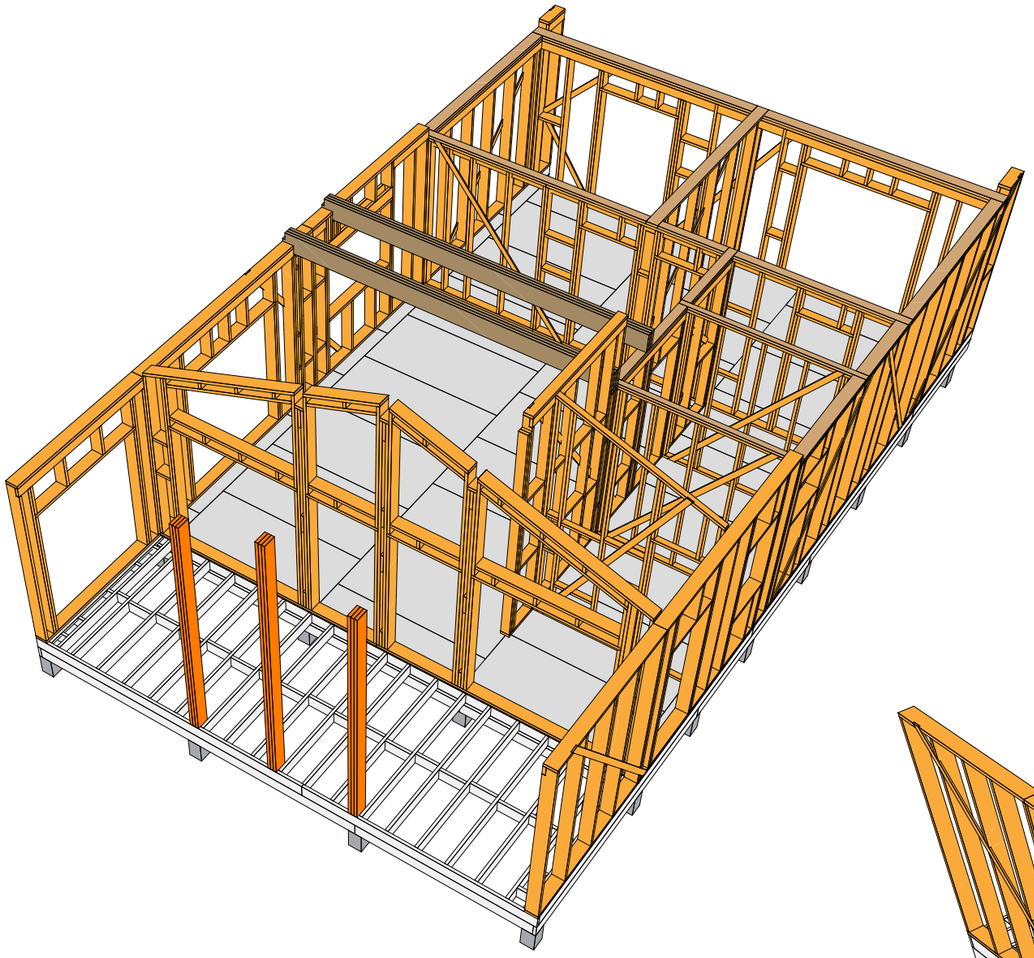

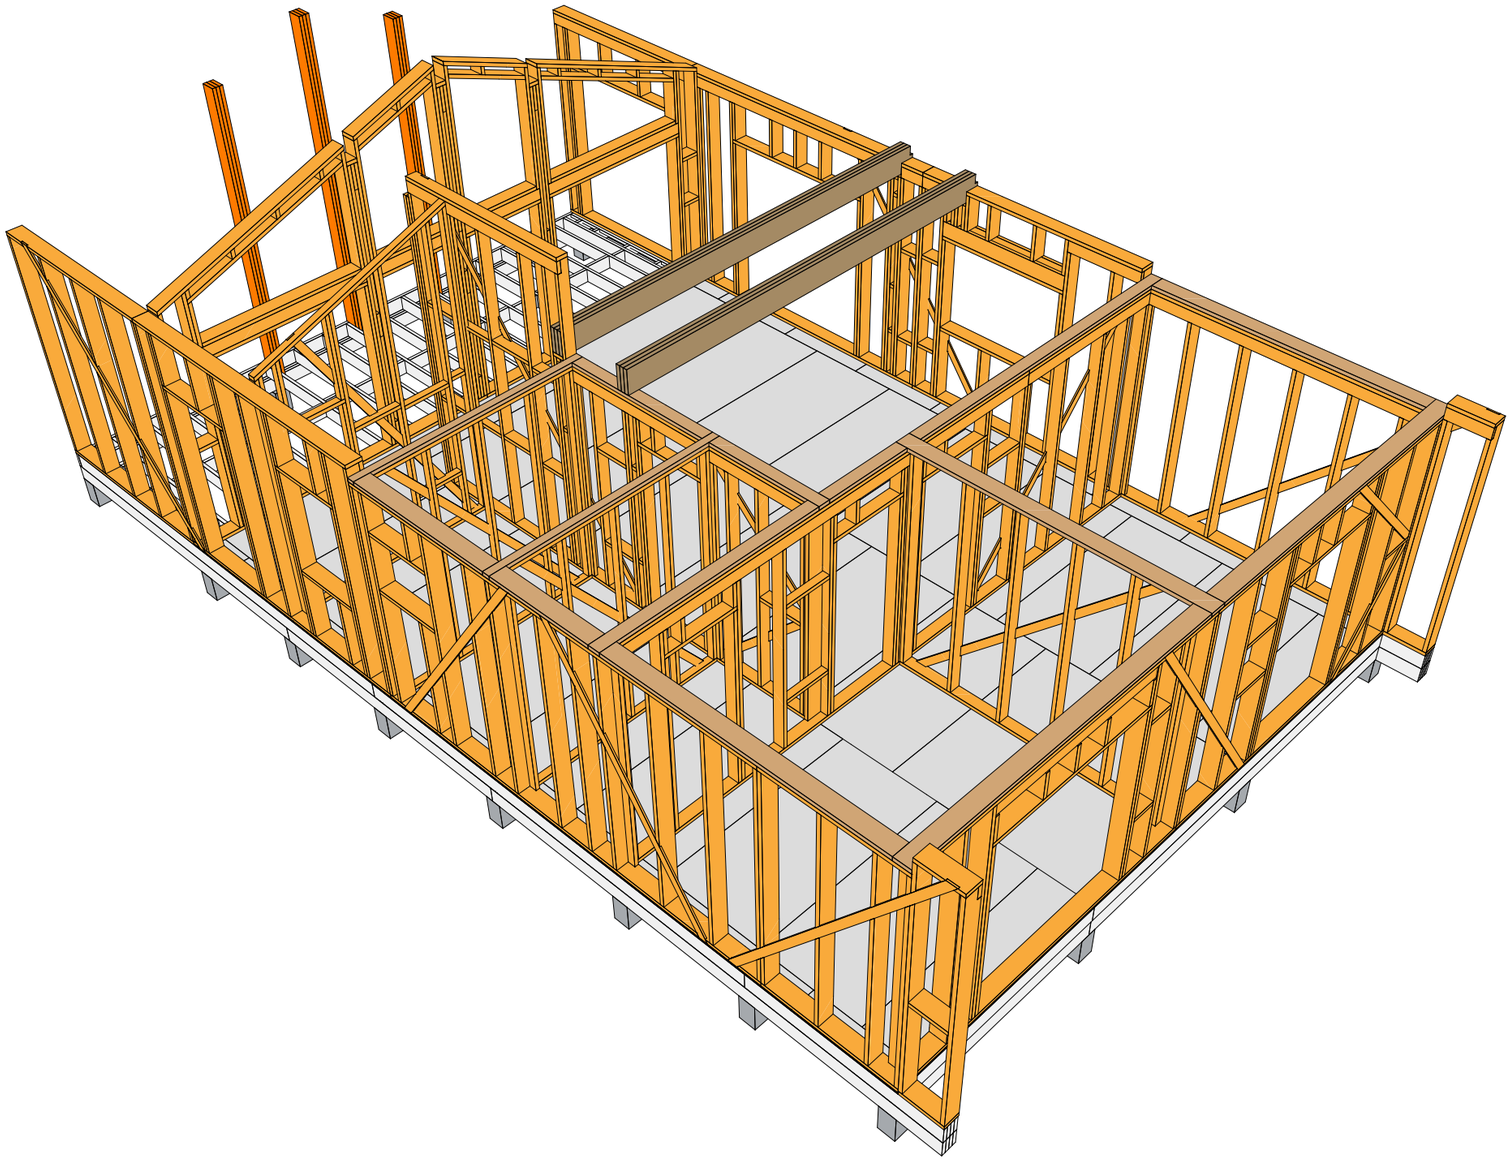

		Подп.	Дата	ИНДИВИДУАЛЬНЫЙ ЖИЛОЙ ДОМ Московская обл. Наро Фоминский район. д. Новоселки	26-03.121-ОМЖБ-13,4х8-103	Модель стен 1 этажа	Лист	Листов	ЭКО КАРКАС
Разраб.	Фадеев С.А.		15.03.2026				22	57	
Пров.			15.03.2026		Раздел КД				