Спецификация опорных конструкций 1-го этажа			
Сечение, мм	Поз.	Длина, мм	Кол-во, шт.
50х300			
	К1	5 335	6
			6

Примечание:
1. Перед подъемом опорных балок 1-го этажа необходимо заранее выполнить вырезы, согласно виду в разрезе на этом листе.
2. Опорная балка устанавливается, после монтажа второй верхней обвязки 1-го этажа.
3. Высоту опорной балки смотри разрез 3-3, лист 53

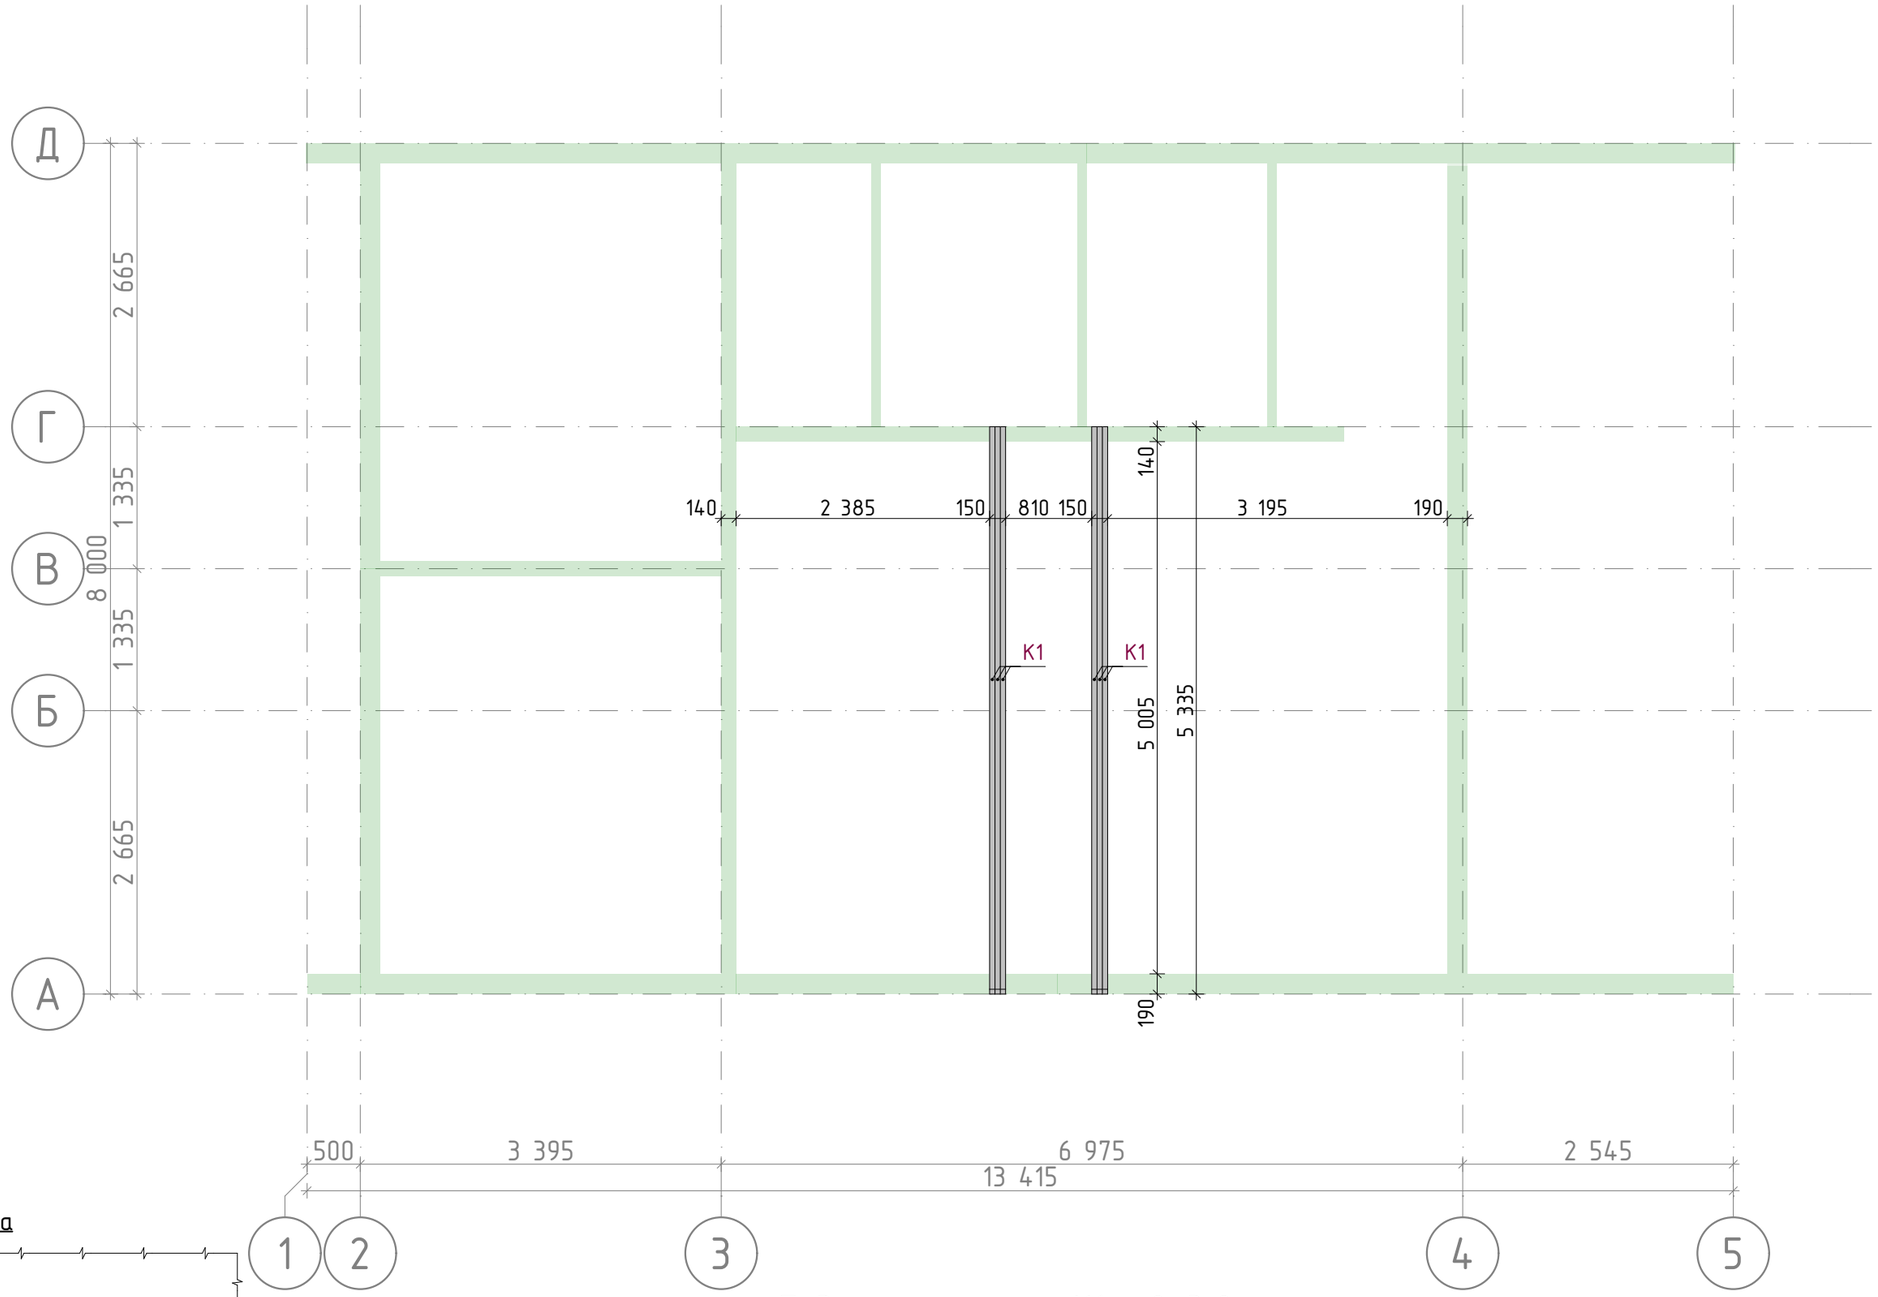

Опорная балка 1-го этажа

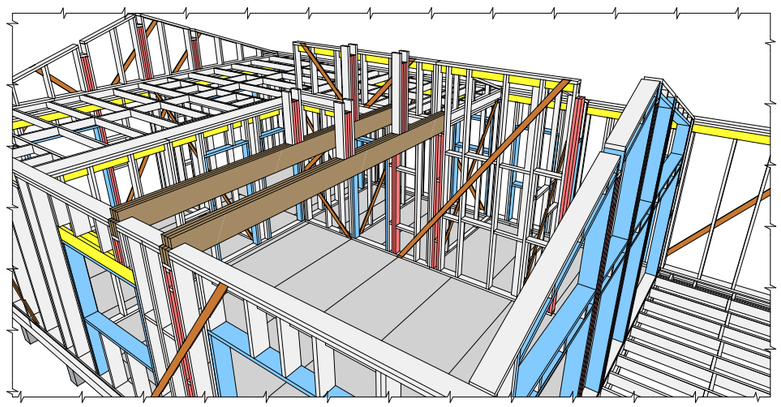

Подрезка элемнта К1 - вид в разрезе

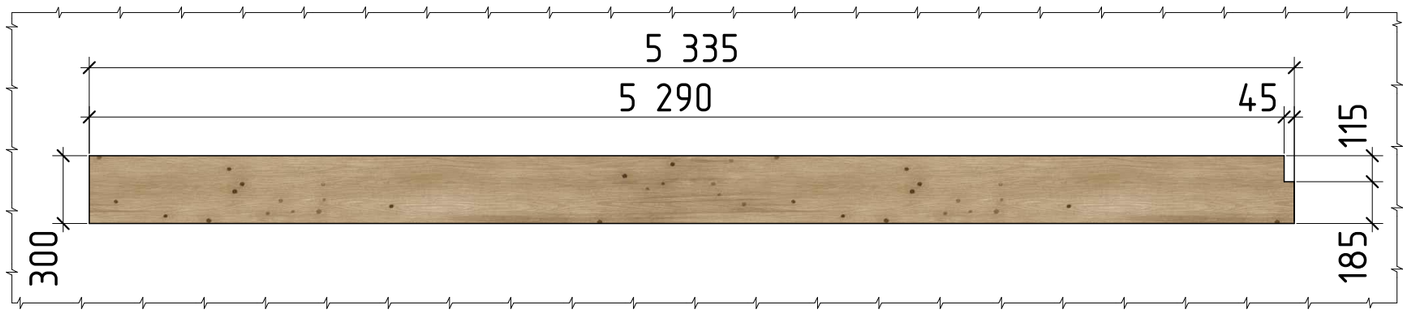

		Подп.	Дата	ИНДИВИДУАЛЬНЫЙ ЖИЛОЙ ДОМ Московская обл. Наро Фоминский район. д. Новоселки	26-03.121-ОМЖБ-13,4х8-103	Схема монтажа опорных конструкций 1-го этажа	Лист	Листов	ЭКО КАРКАС
Разраб.	Фадеев С.А.		15.03.2026				37	57	
Пров.			15.03.2026		Раздел КД				