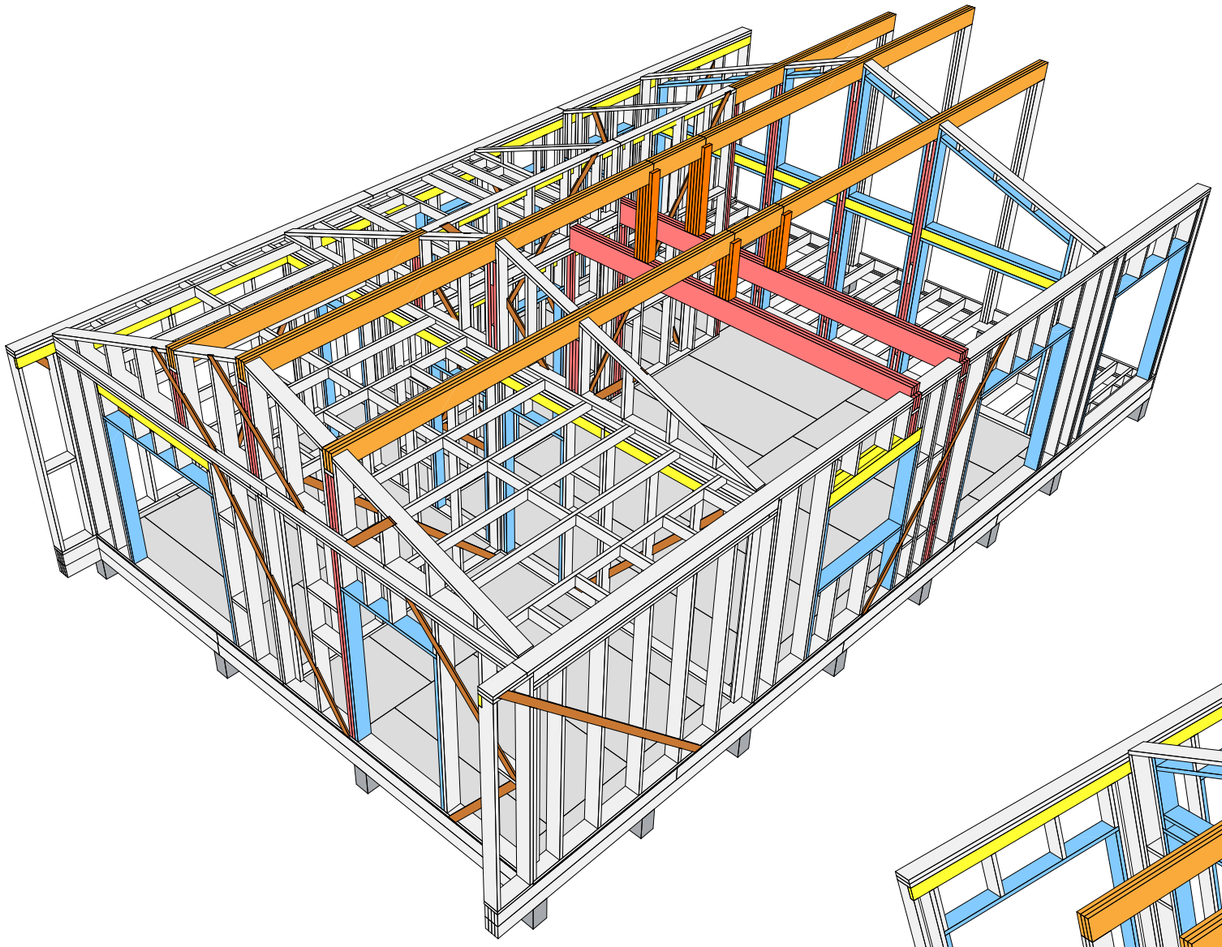

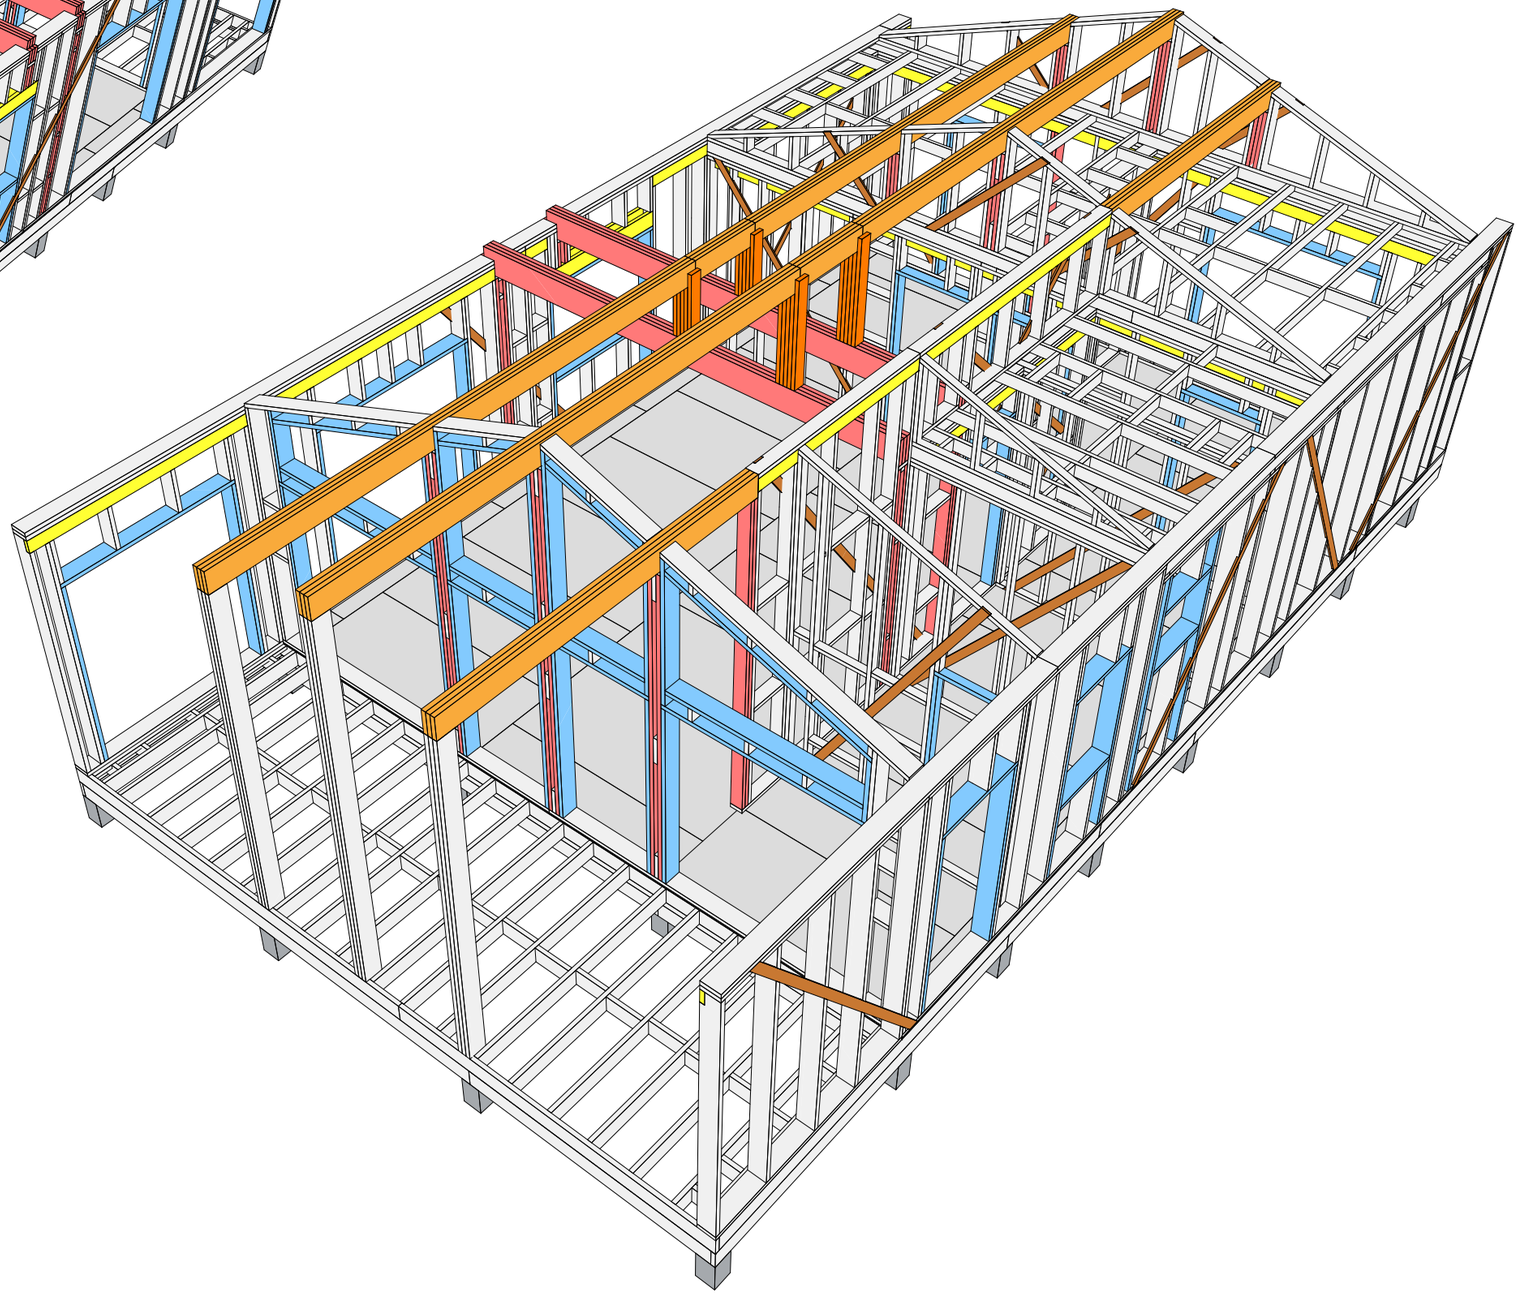

		Подп.	Дата	ИНДИВИДУАЛЬНЫЙ ЖИЛОЙ ДОМ Московская обл. Наро Фоминский район. д. Новоселки	26-03.121-ОМЖБ-13,4х8-103		Модель опорных конструкций строп. системы	Лист	Листов	ЭКО КАРКАС
Разраб.	Фадеев С.А.		15.03.2026					48	57	
Пров.			15.03.2026		Раздел	КД				